


PROESTIMATOR AI

SAMPLE CONSTRUCTION DOCUMENT SET

3-story commercial mixed-use · 28,400 GSF · Class B occupancy

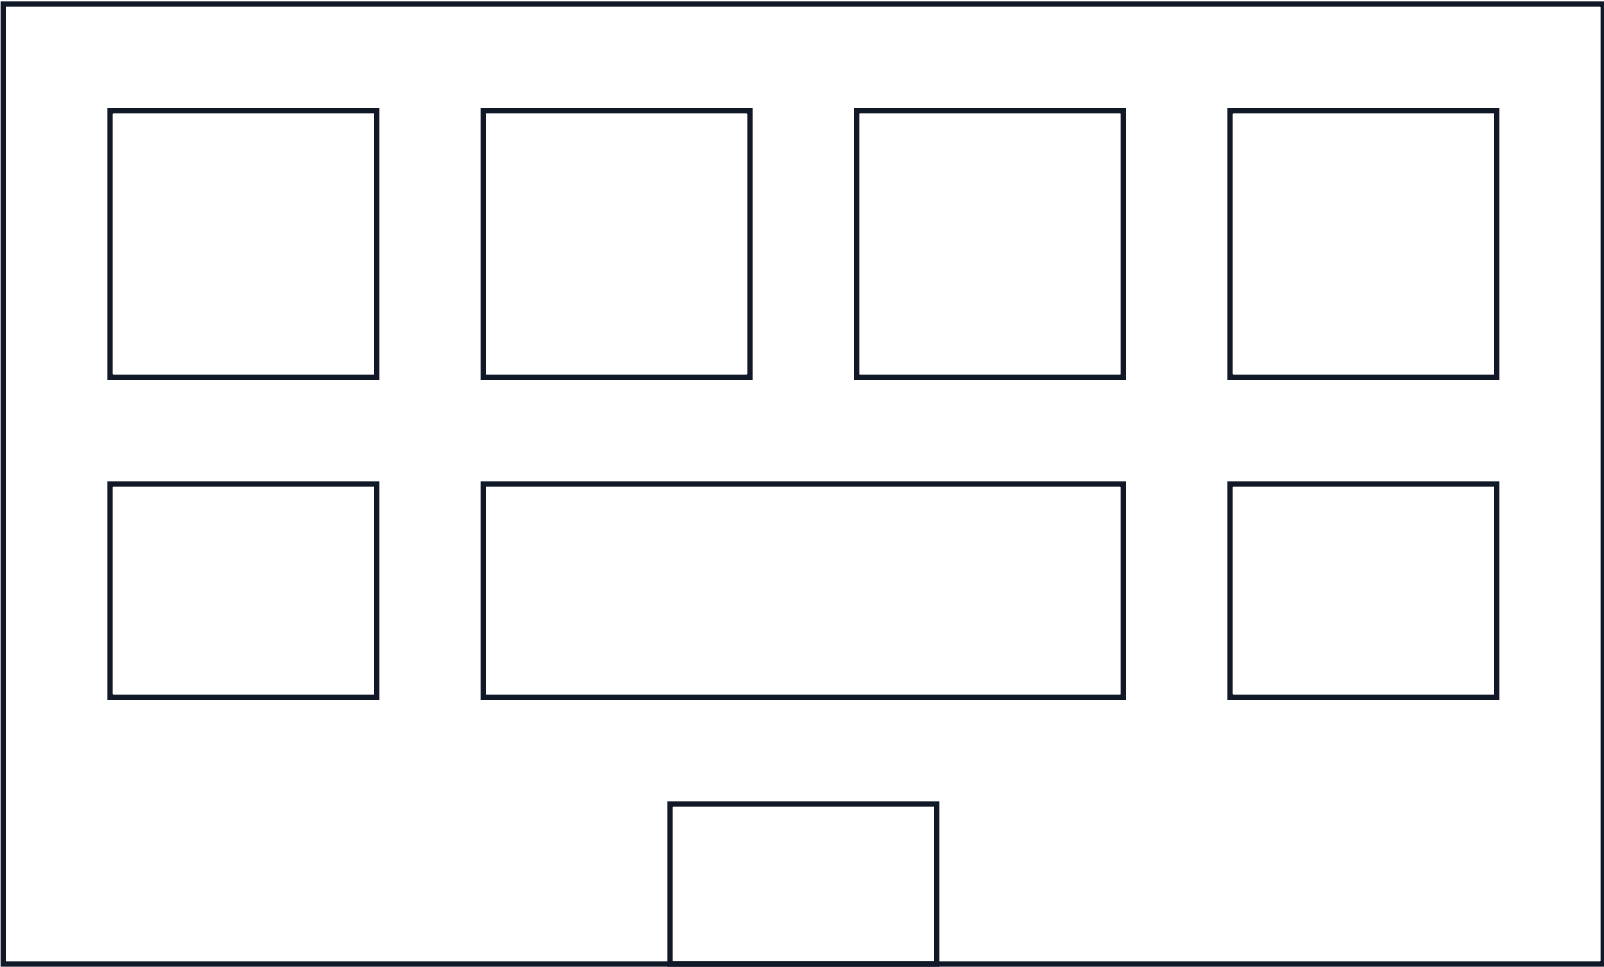

This is a synthetic fixture document. All dimensions, room names, and quantities are illustrative.

LEVEL 1 · FIRST FLOOR PLAN

200'-0"

DRAWN TO SCALE 1/4" = 1'-0"

130'-0"

LOBBY
101

OFFICE A
102

CORRIDOR
C-1

OPEN OFFICE
104

STORAGE
106

RESTROOM
107

ARCHITECTURE

LEVEL 2 · FIRST FLOOR PLAN

200'-0"

DRAWN TO SCALE 1/4" = 1'-0"

130'-0"

EXEC SUITE
201

CONFERENCE
202

CORRIDOR
C-2

BENCH DESKS
204

FILE ROOM
206

RESTROOM
207

ARCHITECTURE


ROOF PLAN

DRAWN TO SCALE 1/4" = 1'-0"

SLOPE 1/4":1' !'	
RD	RD
RD	RD
RD	RD

REFLECTED CEILING PLAN

DRAWN TO SCALE 1/4" = 1'-0"

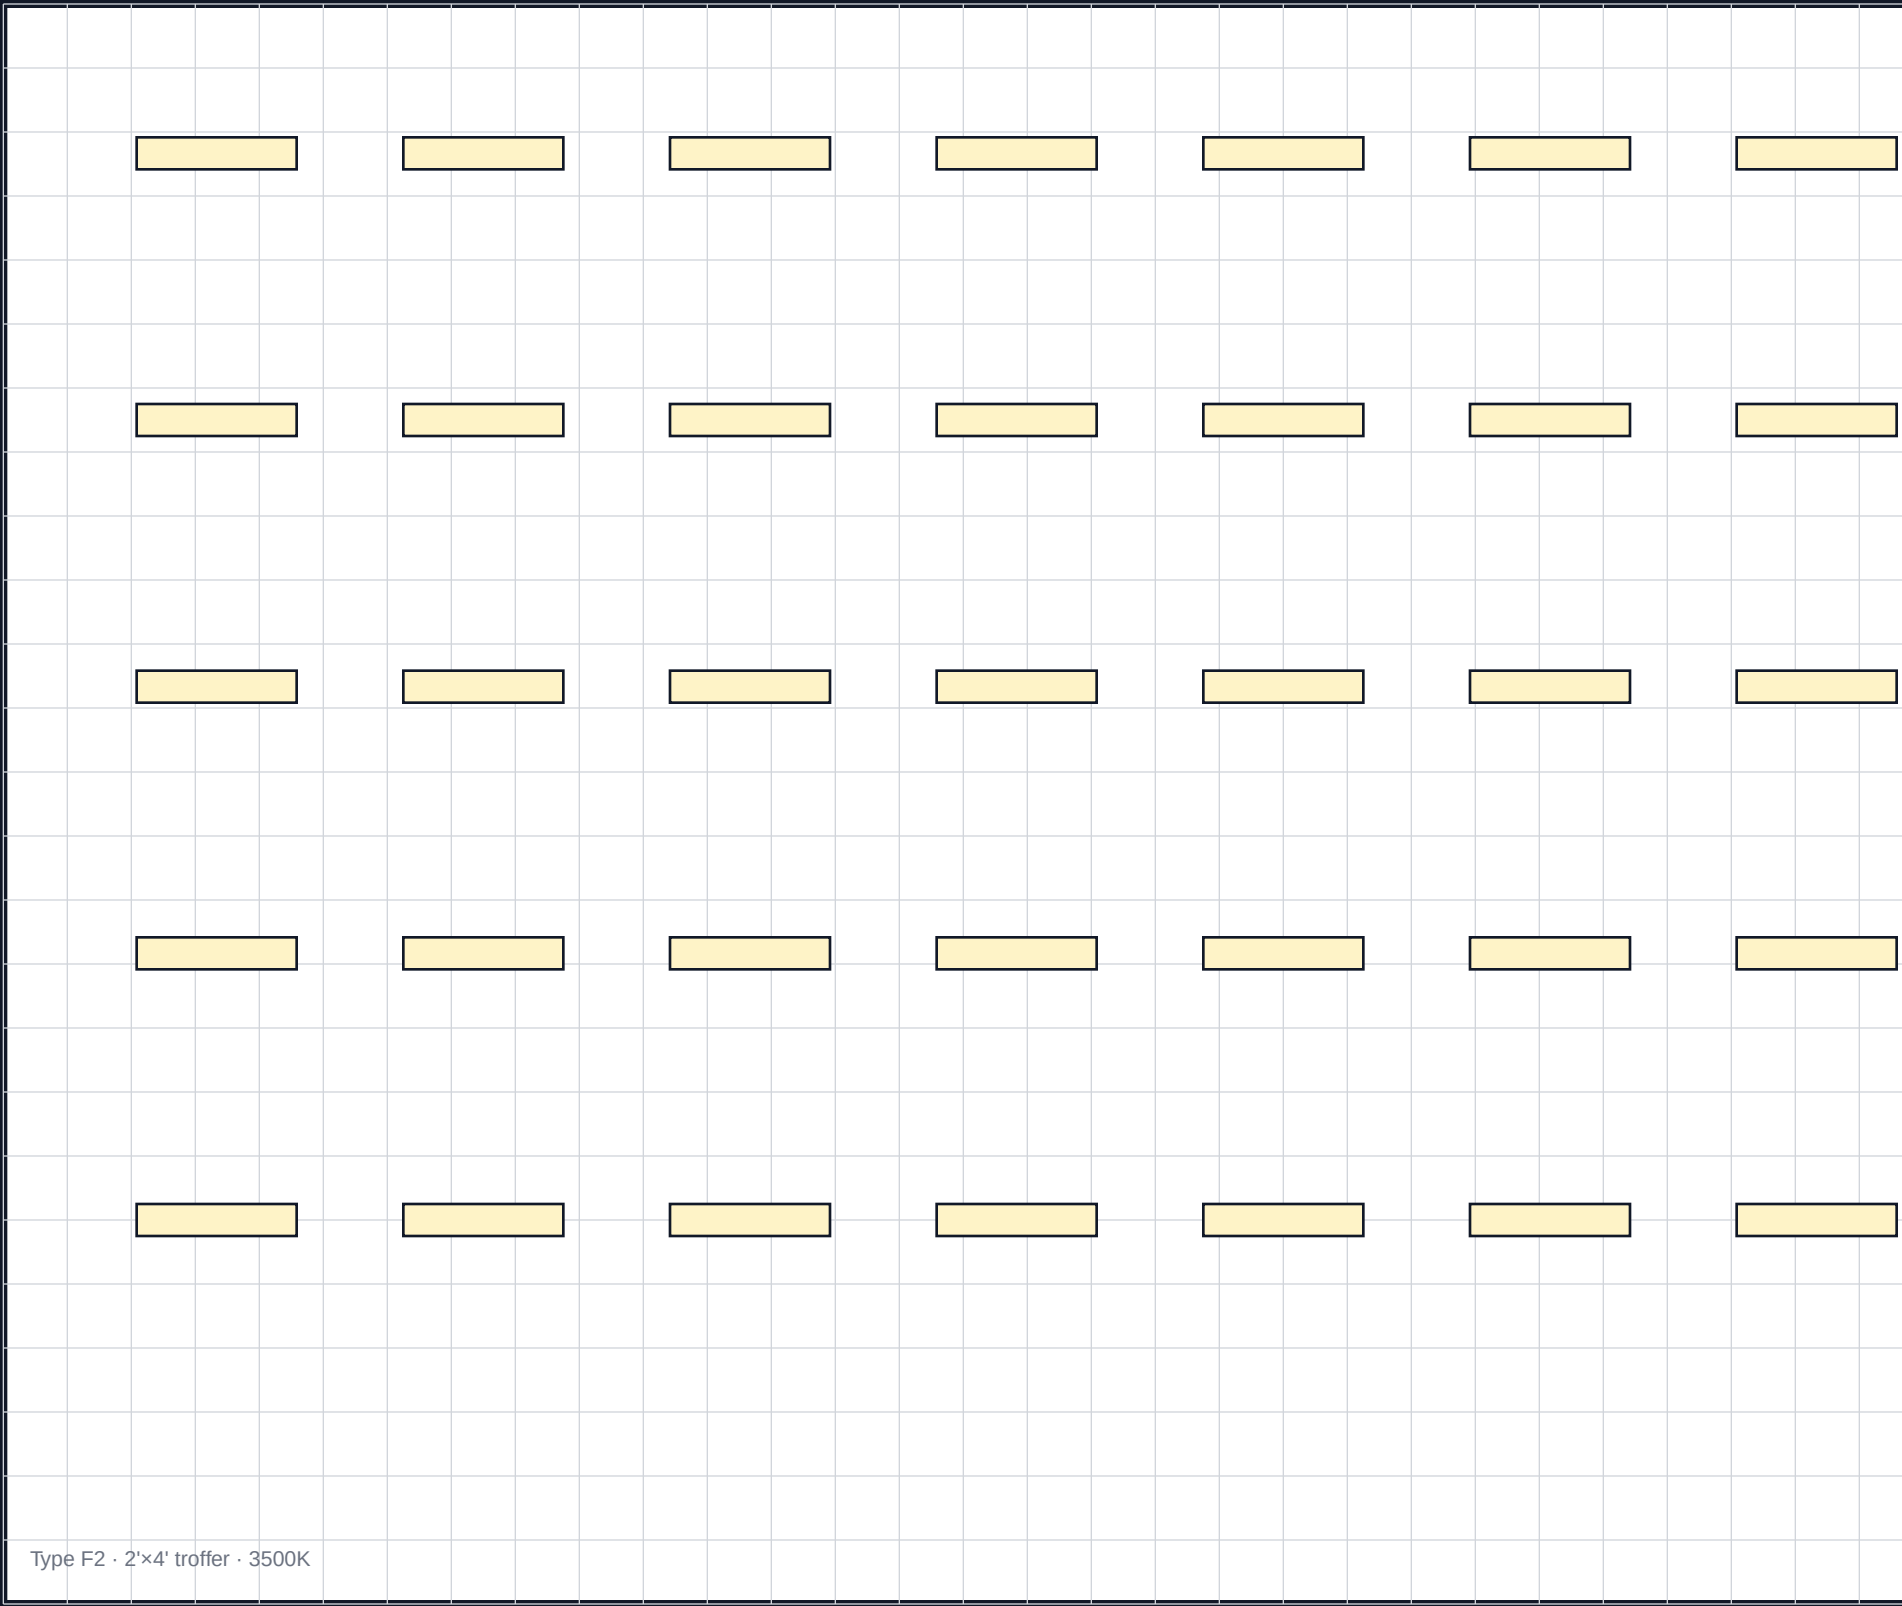

DOOR & WINDOW SCHEDULE

DRAWN TO SCALE 1/4" = 1'-0"

MARK	TYPE	WIDTH	HEIGHT	MATERIAL	HARDWARE	FIRE	FRAME
D-101	Single Leaf	3'-0"	7'-0"	Solid Core Wood	H-1	—	HM
D-102	Single Leaf	3'-0"	7'-0"	Solid Core Wood	H-1	20 min	HM
D-103	Single Leaf	3'-0"	7'-0"	Hollow Metal	H-2	45 min	HM
D-104	Double Leaf	5'-0"	7'-0"	Tempered Glass	H-3	—	Aluminum
D-105	Single Leaf	3'-6"	7'-0"	Solid Core Wood	H-1	20 min	HM
D-106	Single Leaf	3'-0"	7'-0"	Hollow Metal	H-2	60 min	HM
W-101	Storefront	8'-0"	10'-0"	Tempered Glass	—	—	Aluminum
W-102	Punched Opening	4'-0"	5'-0"	Tempered Glass	—	—	Aluminum
W-103	Punched Opening	4'-0"	5'-0"	Tempered Glass	—	—	Aluminum

FOUNDATION PLAN

DRAWN TO SCALE 1/4" = 1'-0"

A

B

C

D

1

F1

F1

F1

F1

2

F1

F1

F1

F1

3

F1

F1

F1

F1

4

F1 - 3'-6" sq footing #5 @ 12" o.c. each way

F1

F1

F1

F1

STRUCTURAL

FRAMING PLAN

DRAWN TO SCALE 1/4" = 1'-0"

A

B

C

D

1

2

3


4

W10x30 beam - A992

STRUCTURAL

HVAC PLAN


DRAWN TO SCALE 1/4" = 1'-0"

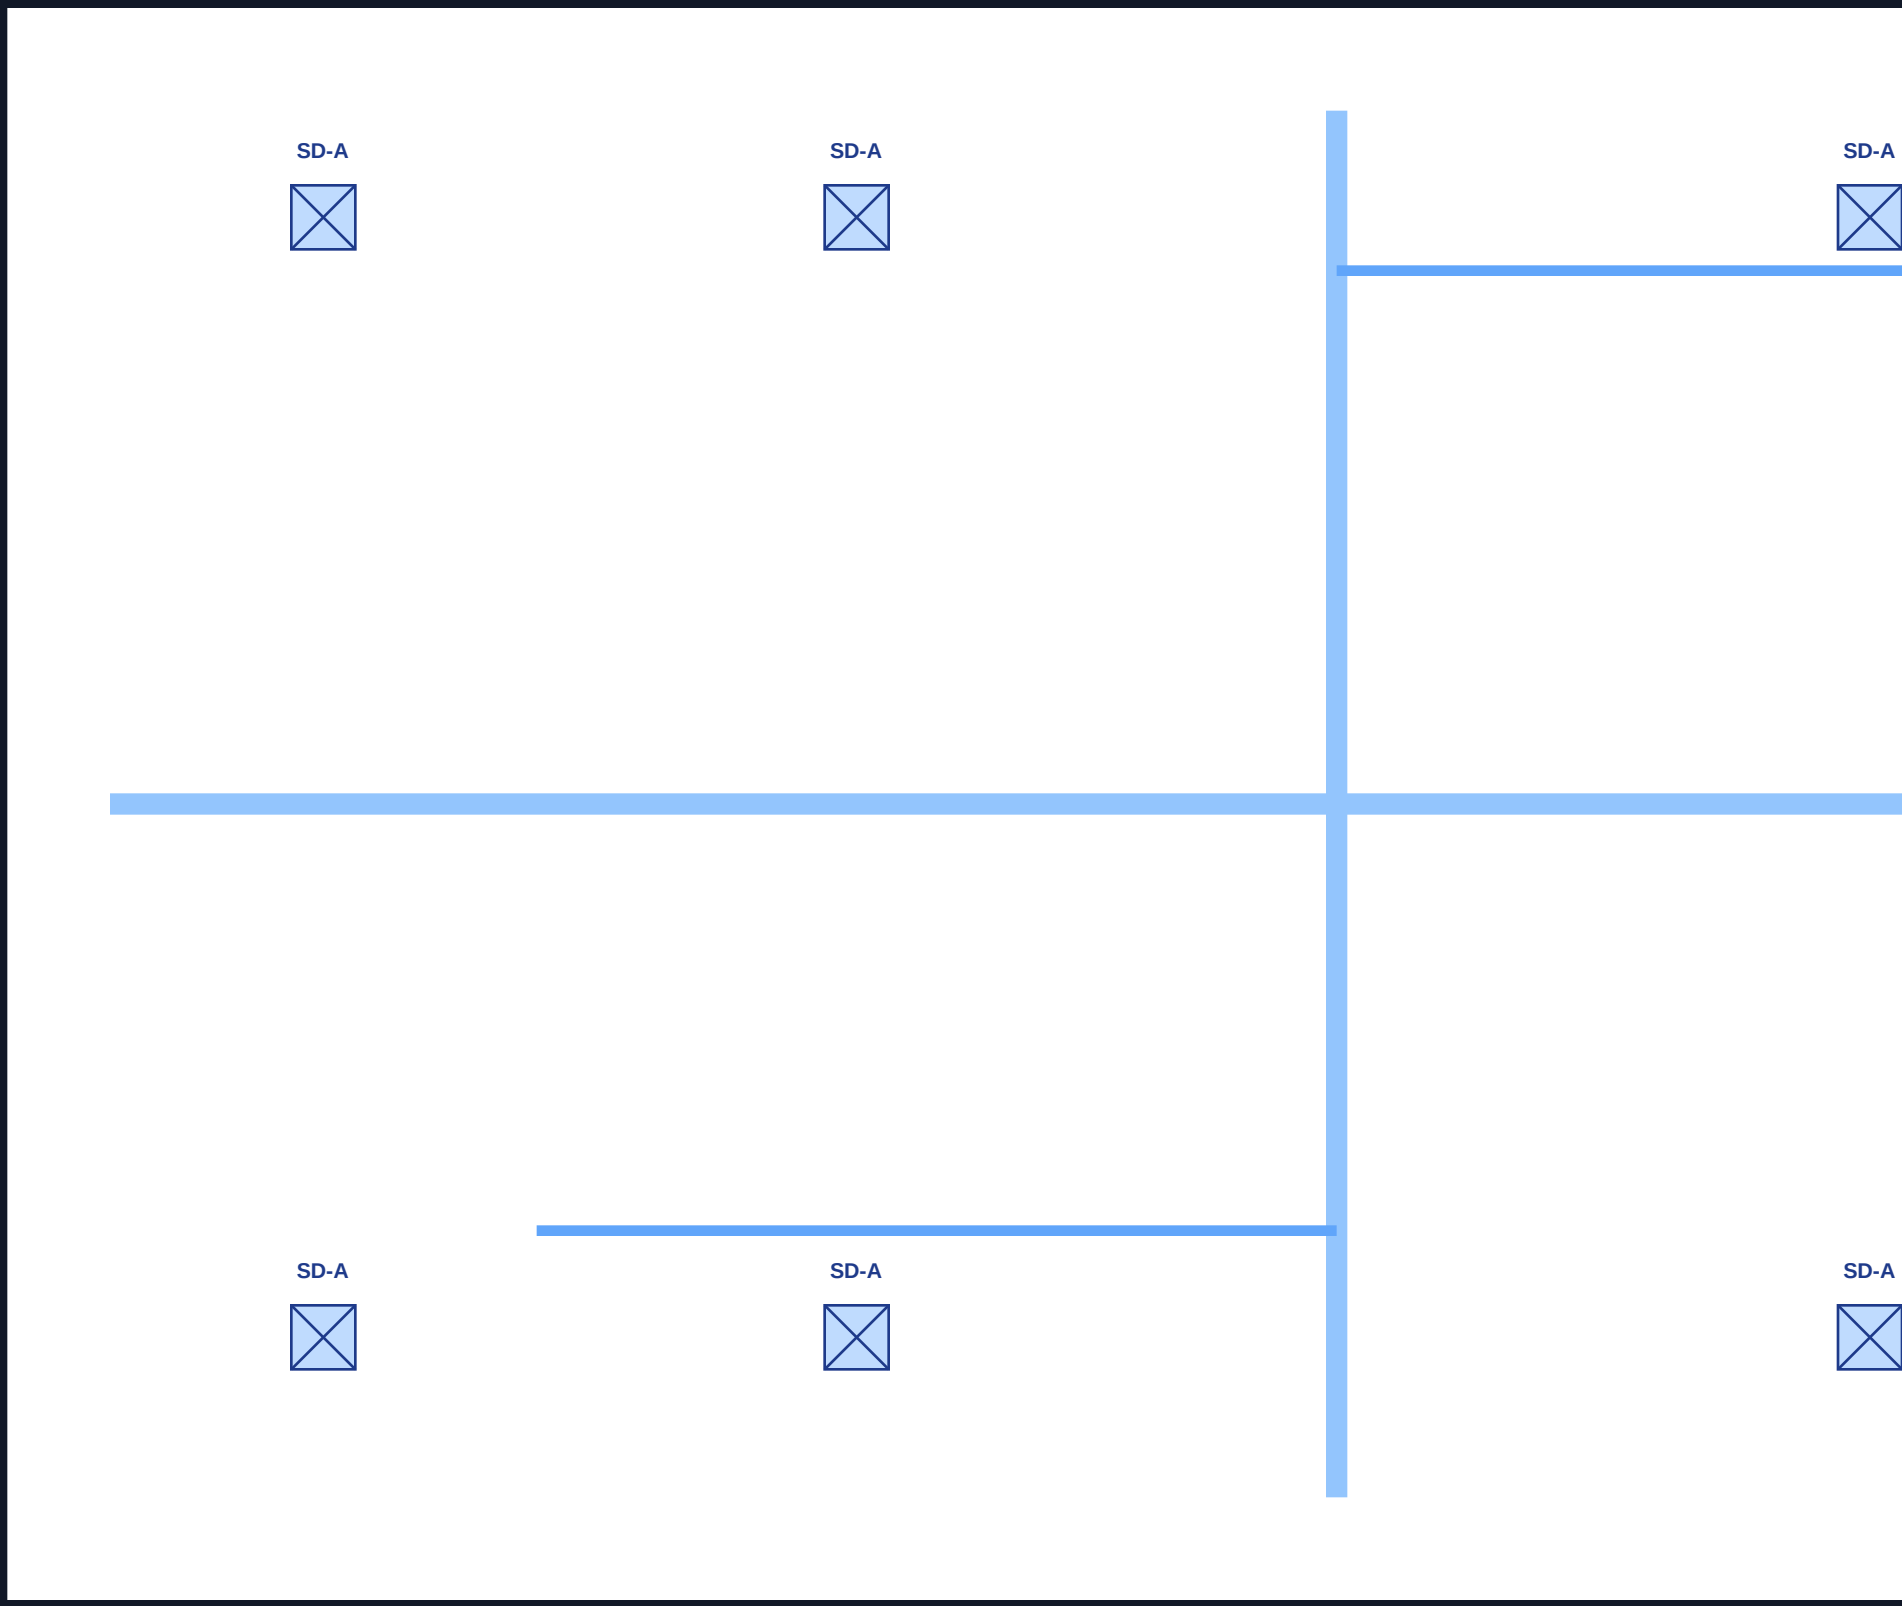

MECHANICAL

POWER PLAN


DRAWN TO SCALE 1/4" = 1'-0"

 

ELECTRICAL

LIGHTING PLAN

DRAWN TO SCALE 1/4" = 1'-0"

 

LECTRICAL

PLUMBING PLAN

DRAWN TO SCALE 1/4" = 1'-0"

